


КОНЦЕПЦИЯ СЦЕНЫ
КУРОРТНОГО КОМПЛЕКСА "ЛУЧИ"

Г. АНАПА


ЭКСПЛИКАЦИЯ ПОМЕЩЕНИЙ

№	НАИМЕНОВАНИЕ	ПЛОЩАДЬ
1	С/У женский	25,74
2	Артмистическая	26,07
3	С/У	8,69
4	Помещение для хранения реквизита	20,61
5	Аппаратная	20,88
6	Артмистическая	25,89
7	С/У	8,68
8	С/У мужской	25,74

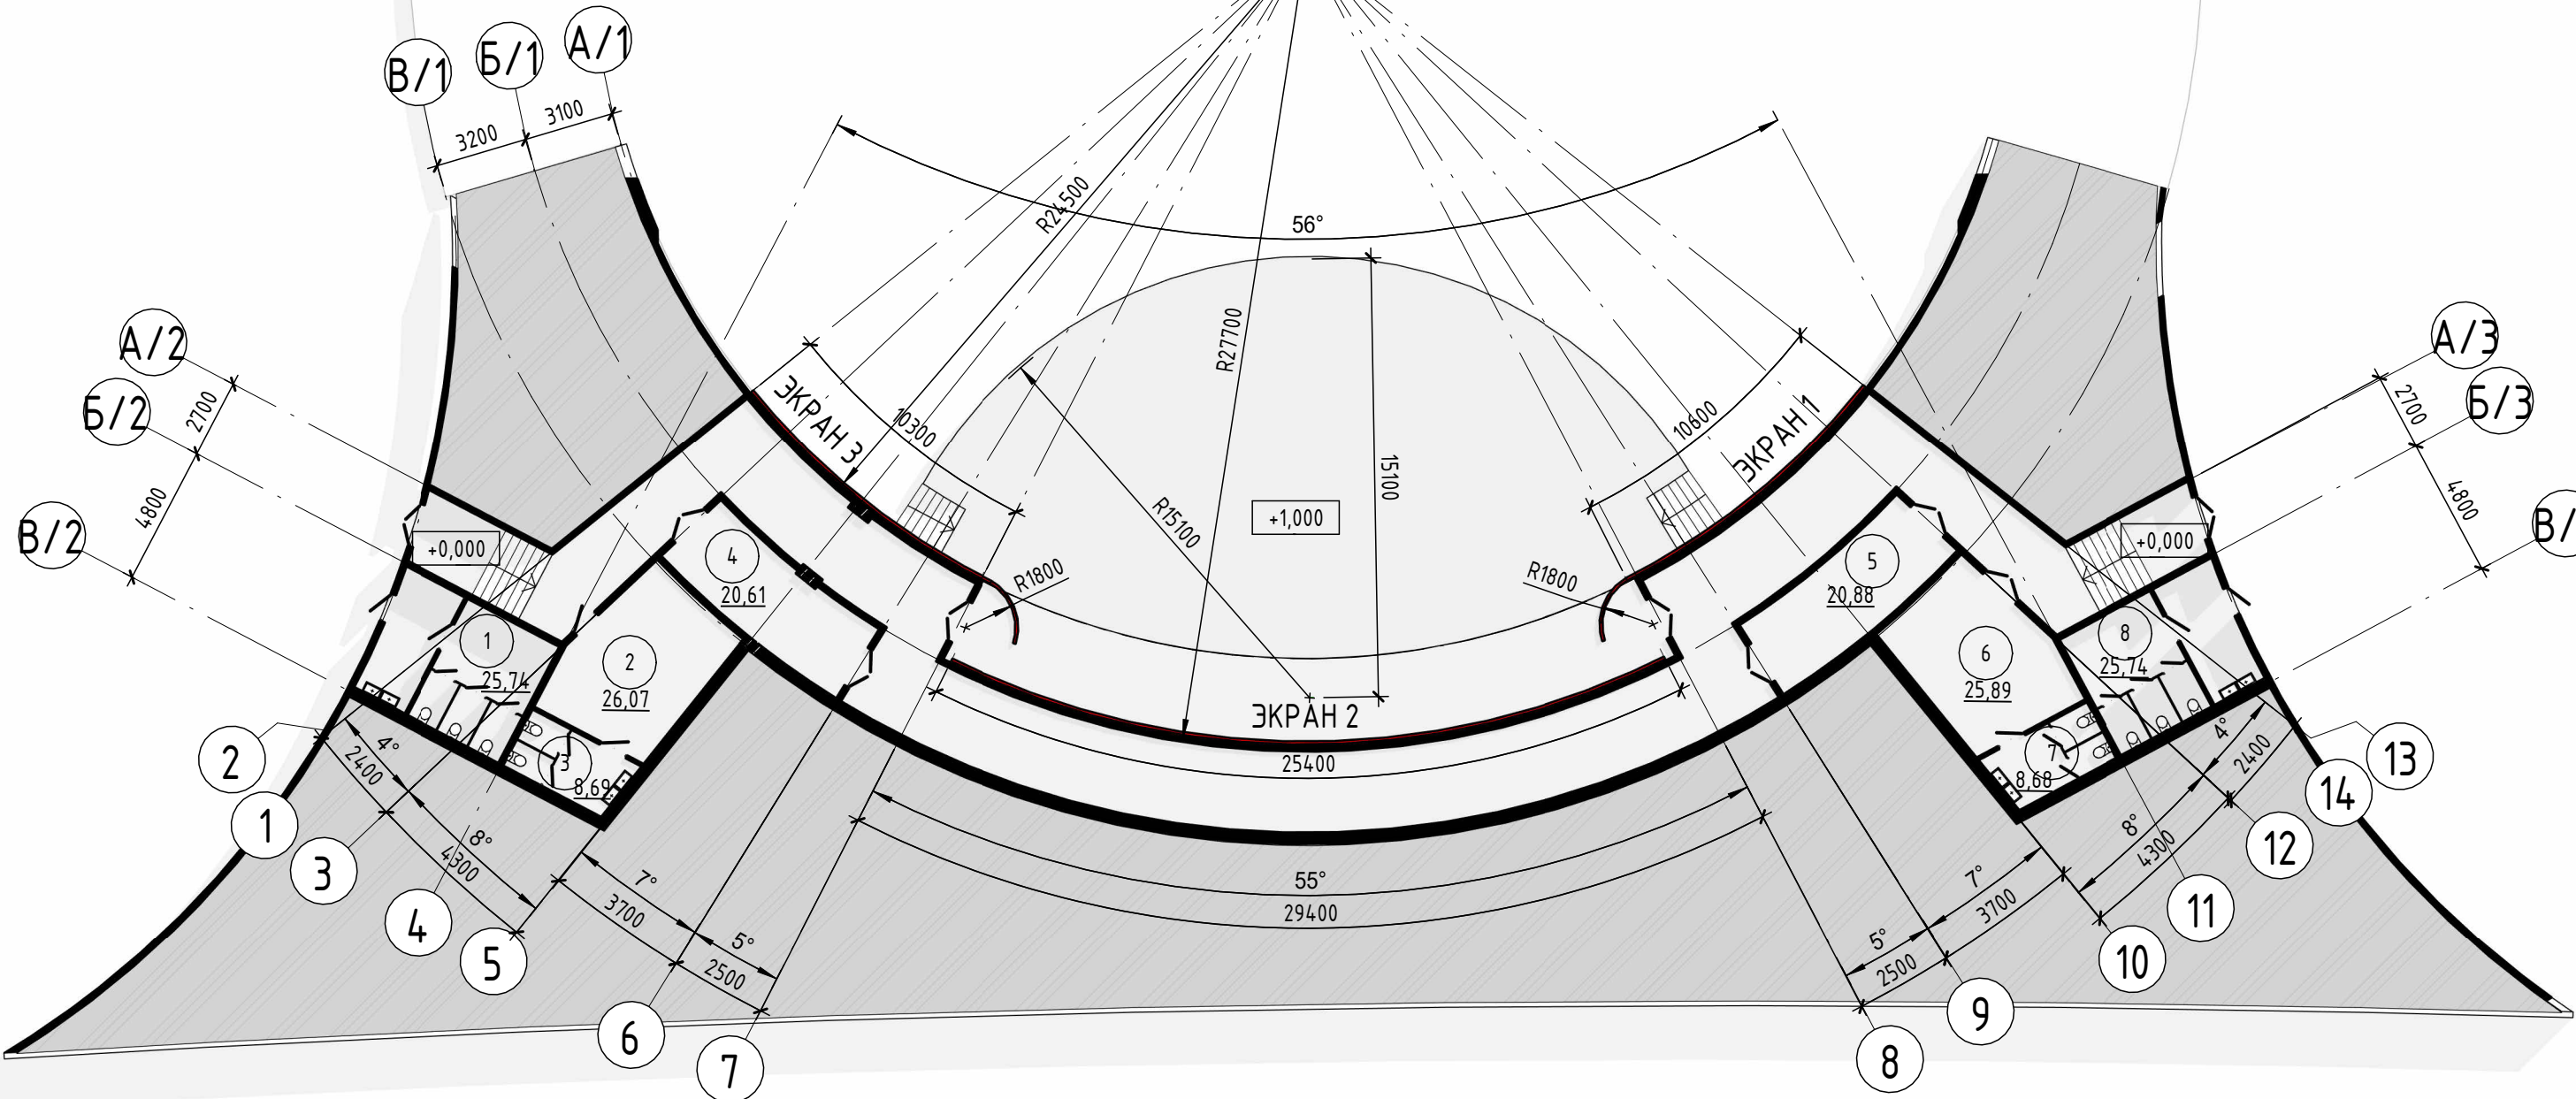


ПЛАН НА ОТМ. +0.450


ФАСАД В ОСЯХ 14-1

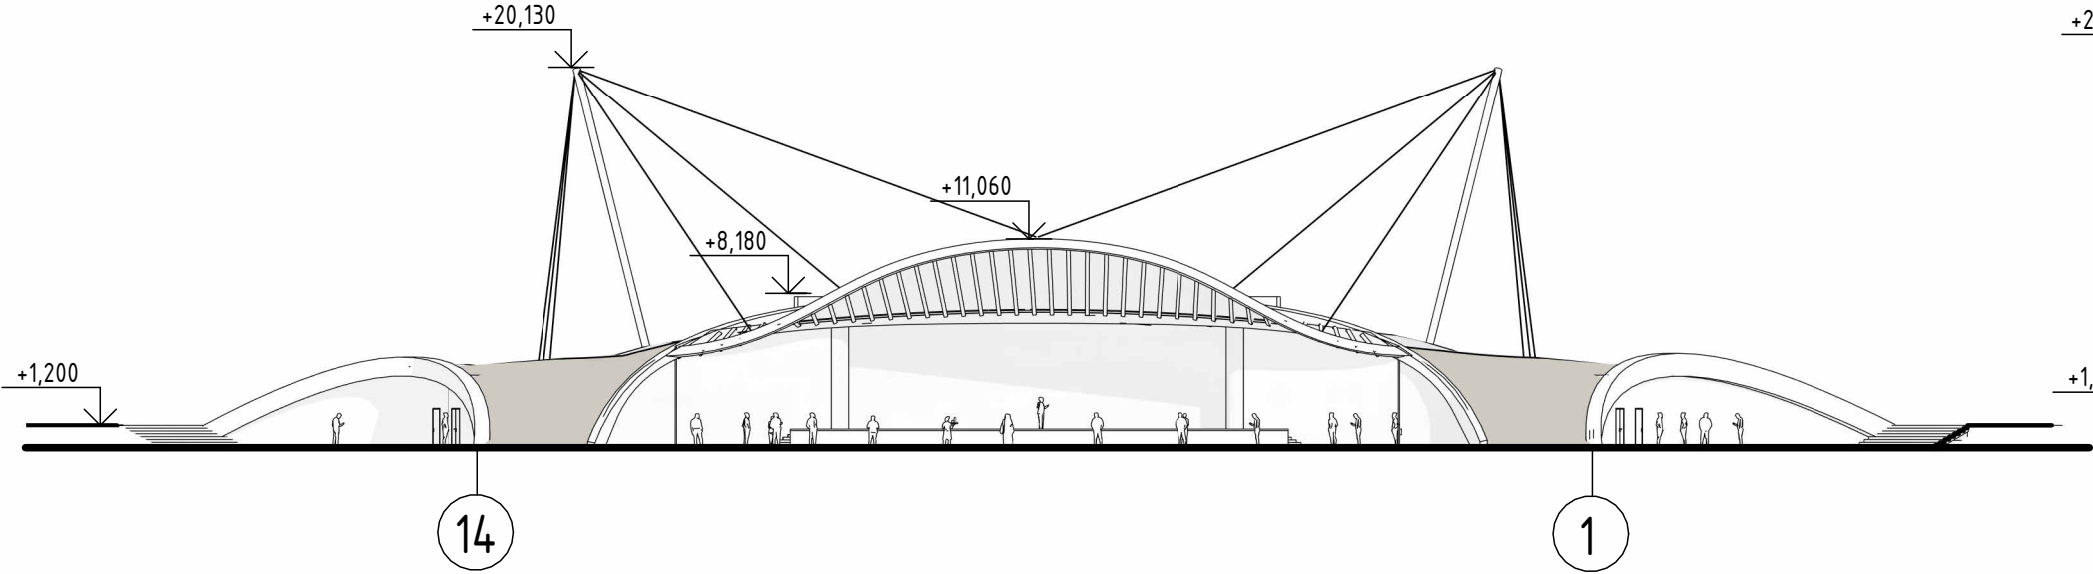


ФАСАД В ОСЯХ В/З-А/1


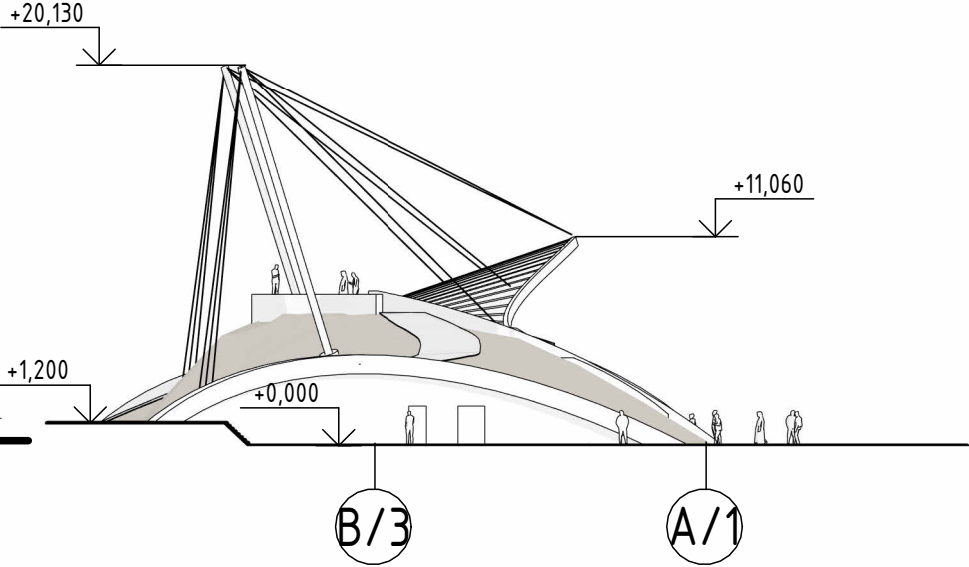


ФАСАД В ОСЯХ 1-14

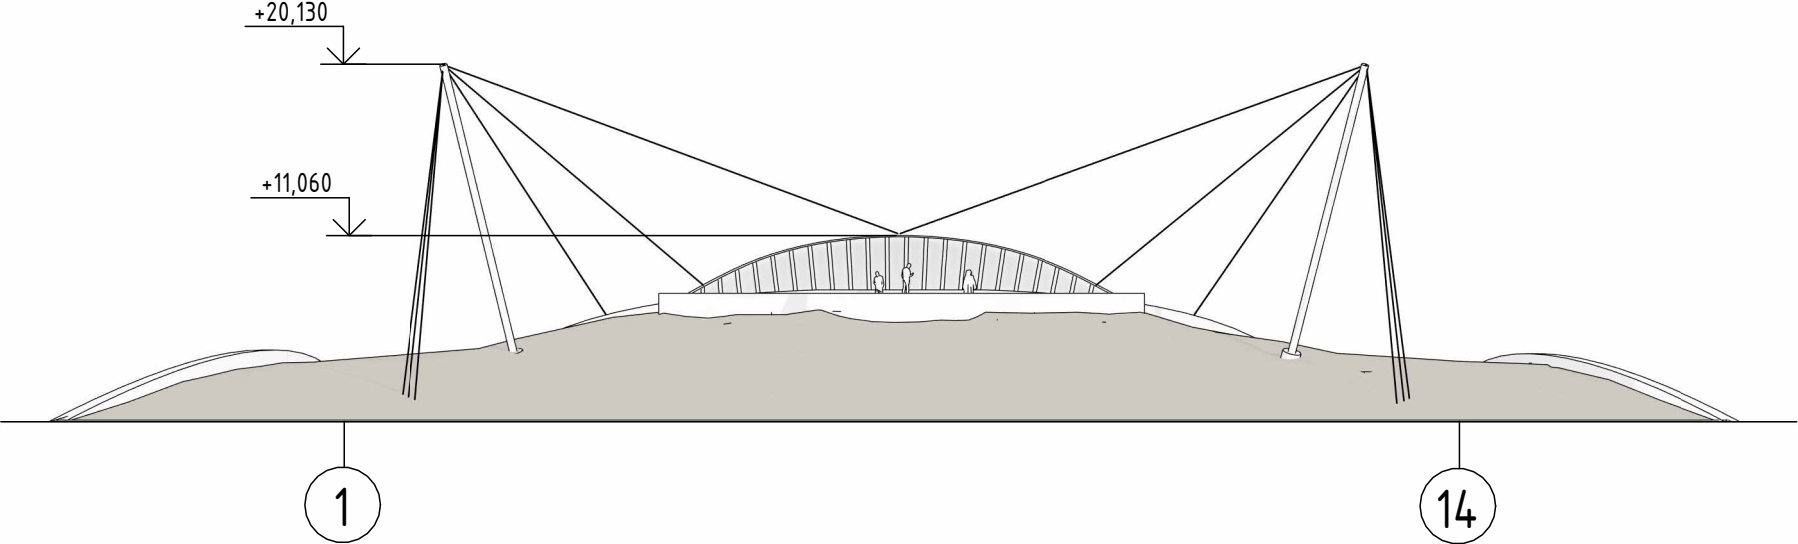

РАЗРЕЗ 1-1

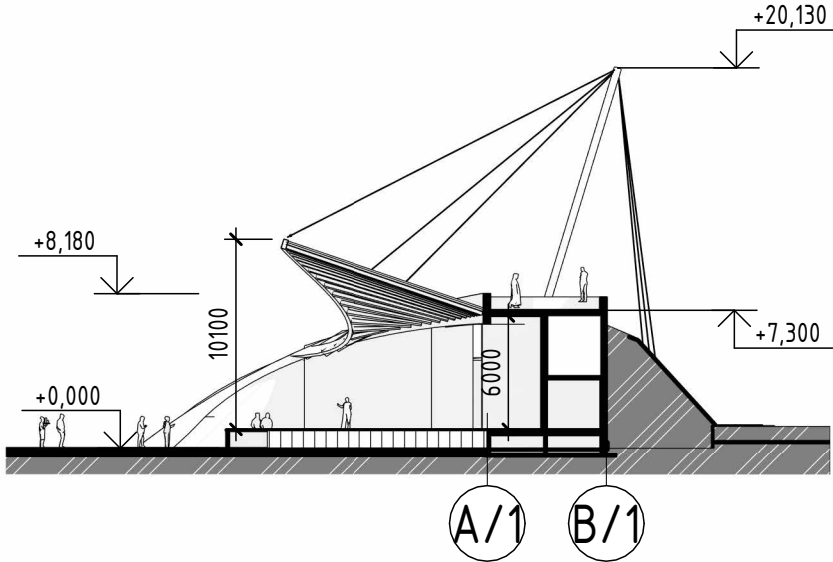

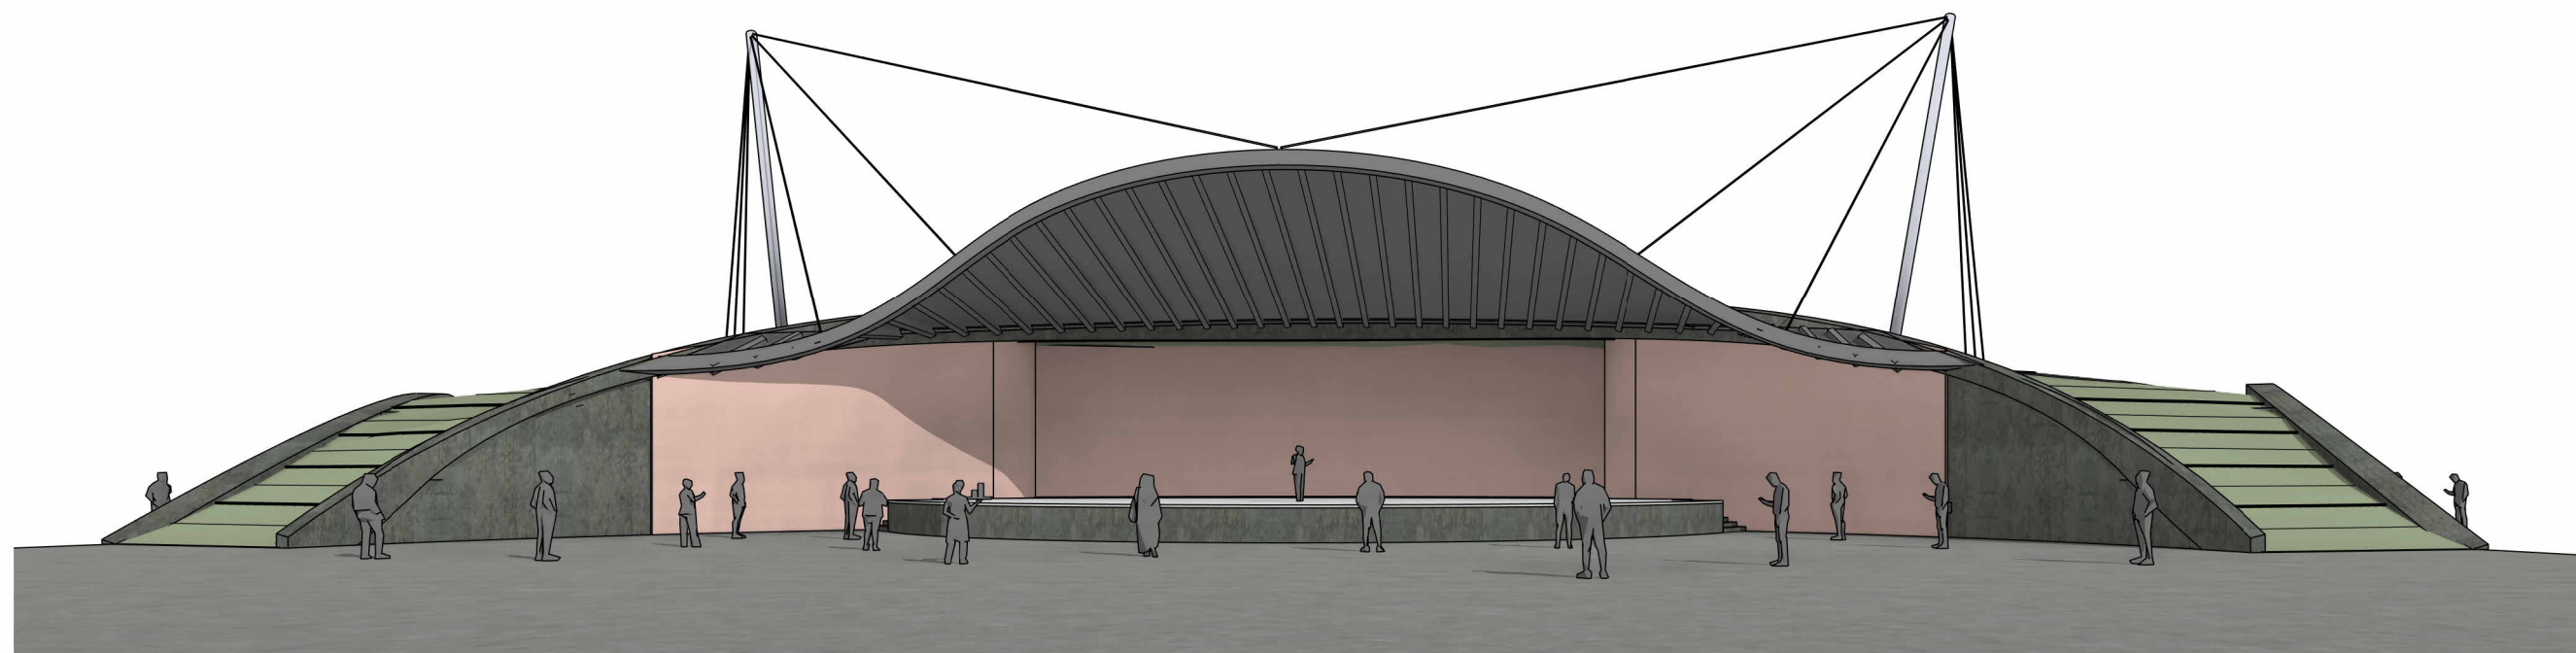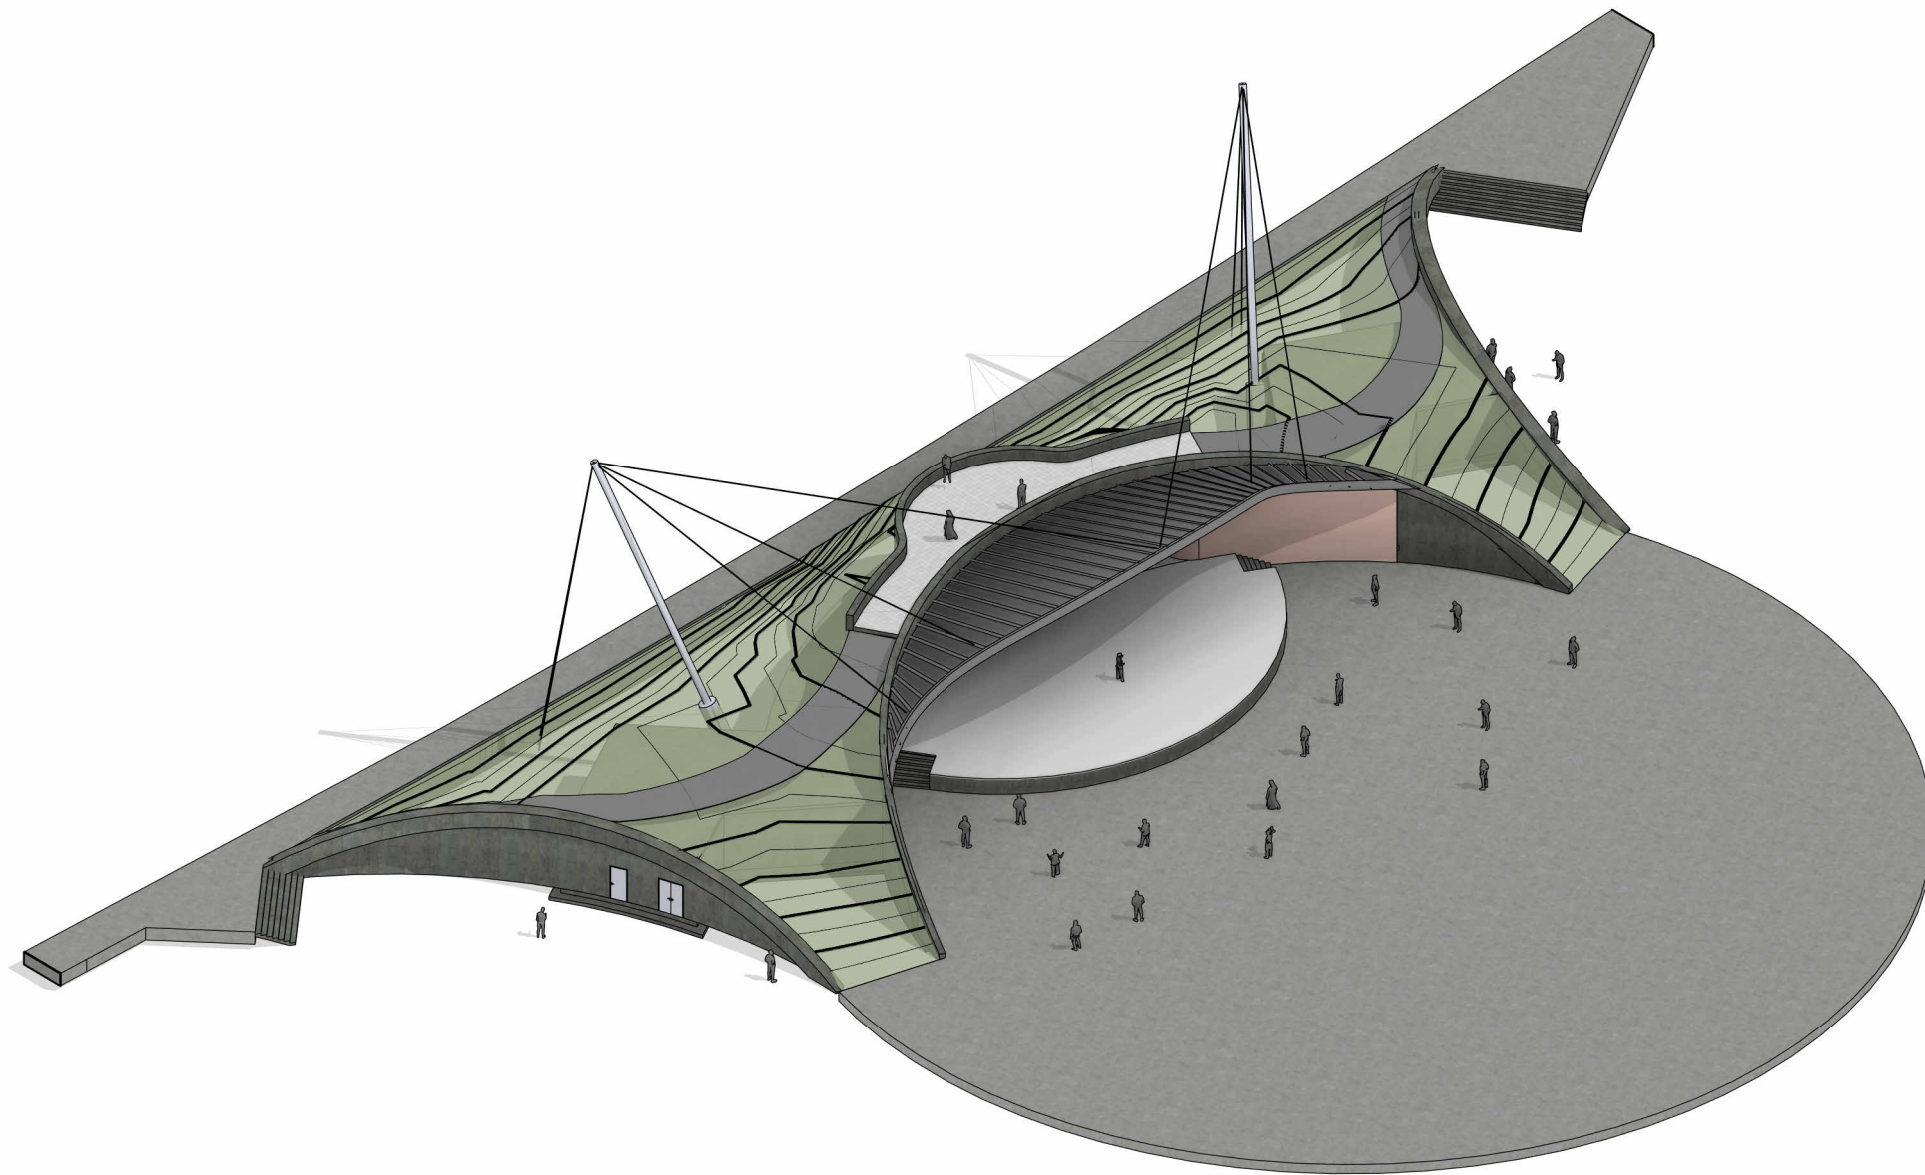


3D ВИДЫ


АРХИТЕКТУРНАЯ
ДОКУМЕНТАЦИЯ

03

ПЛАН

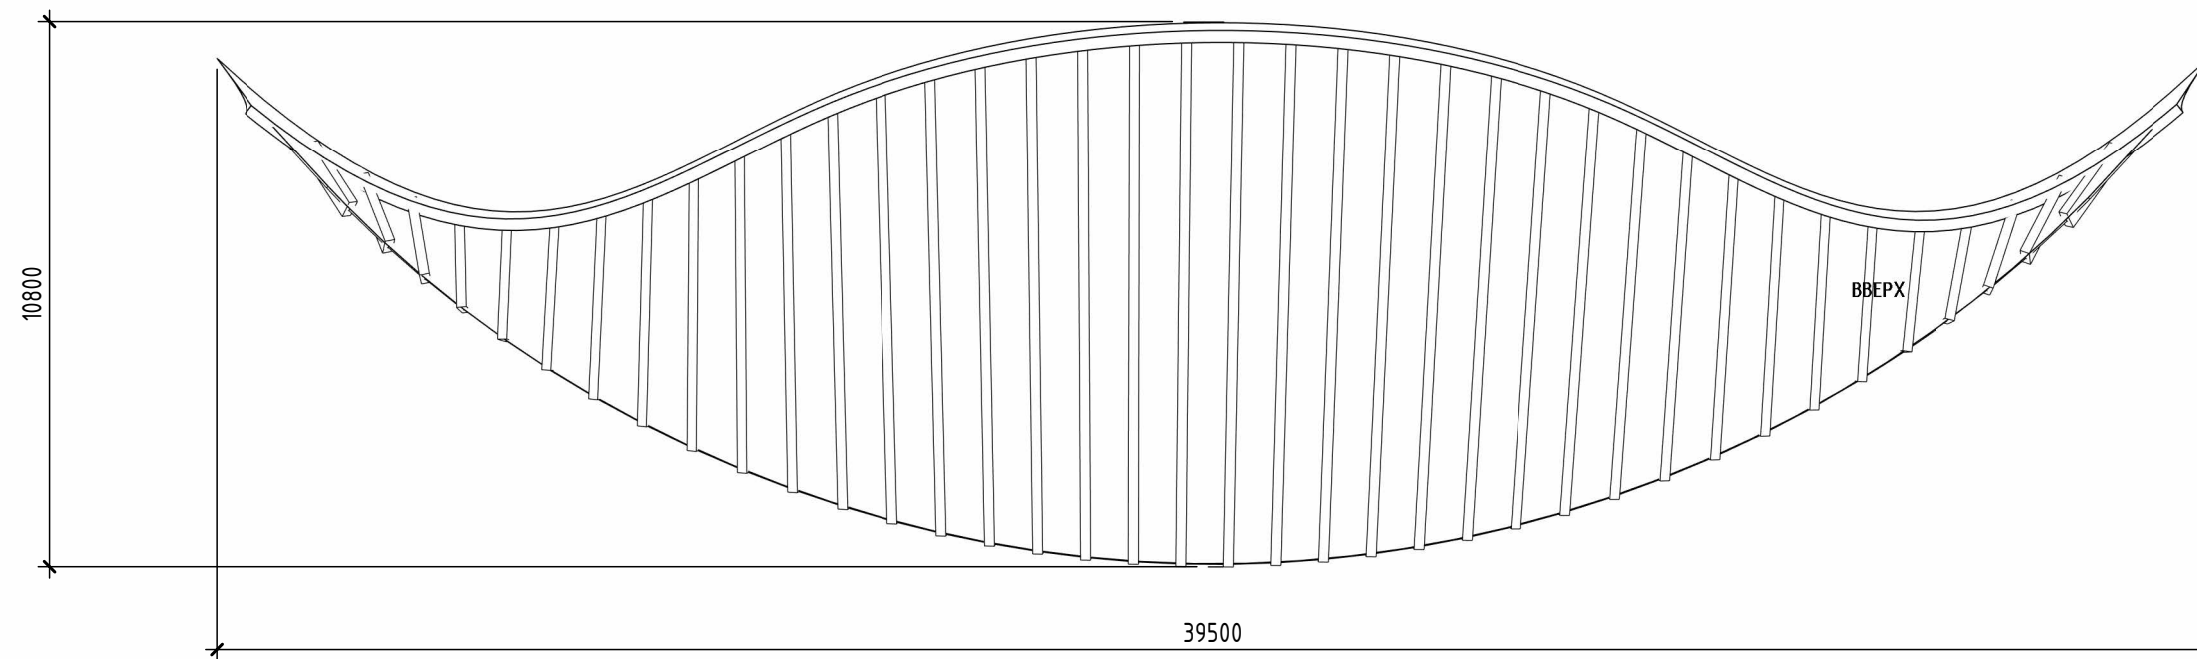


ФАСАД

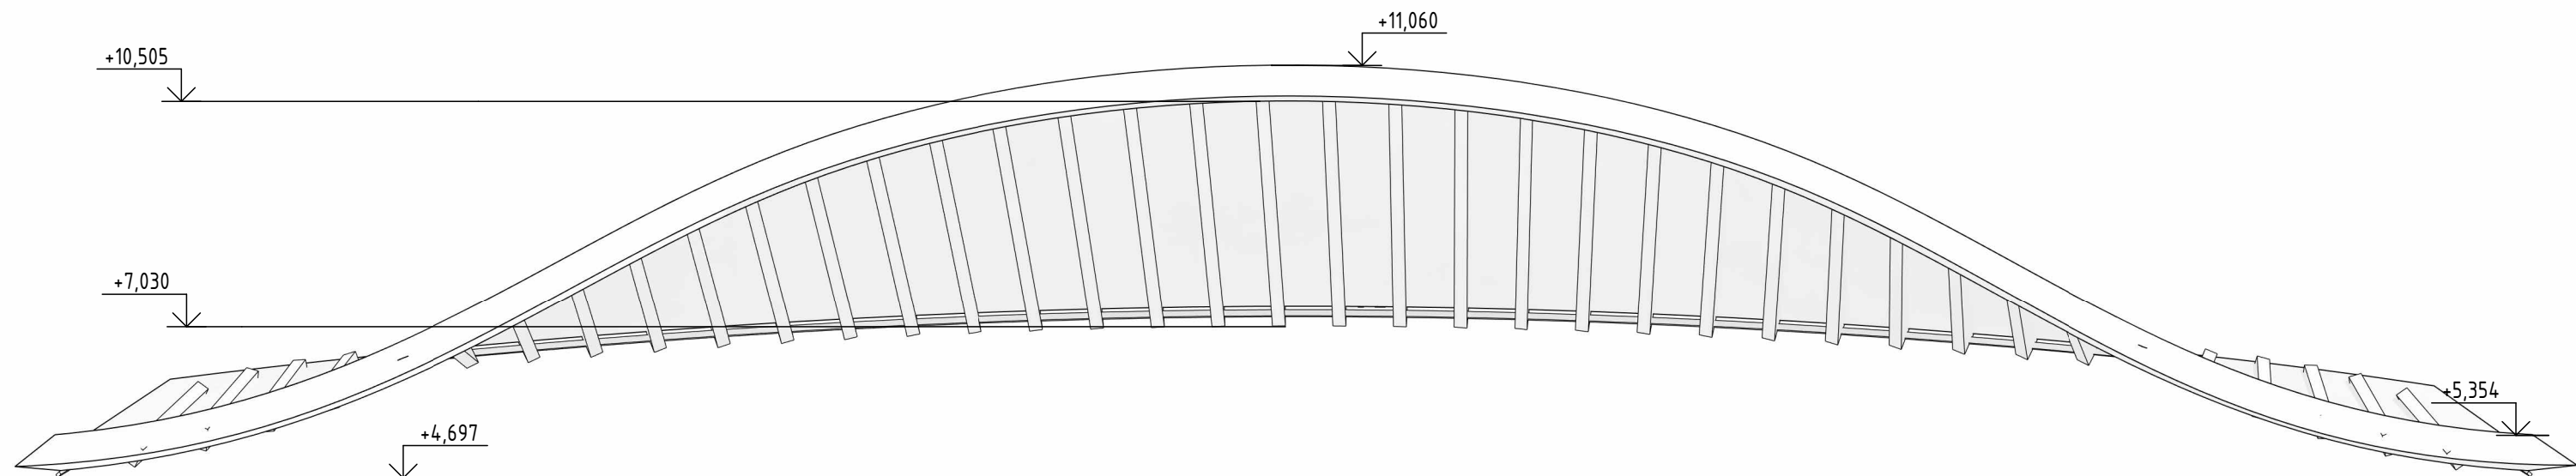

КОНСТРУКЦИЯ НАВЕСА

АРХИТЕКТУРНАЯ
ДОКУМЕНТАЦИЯ

04

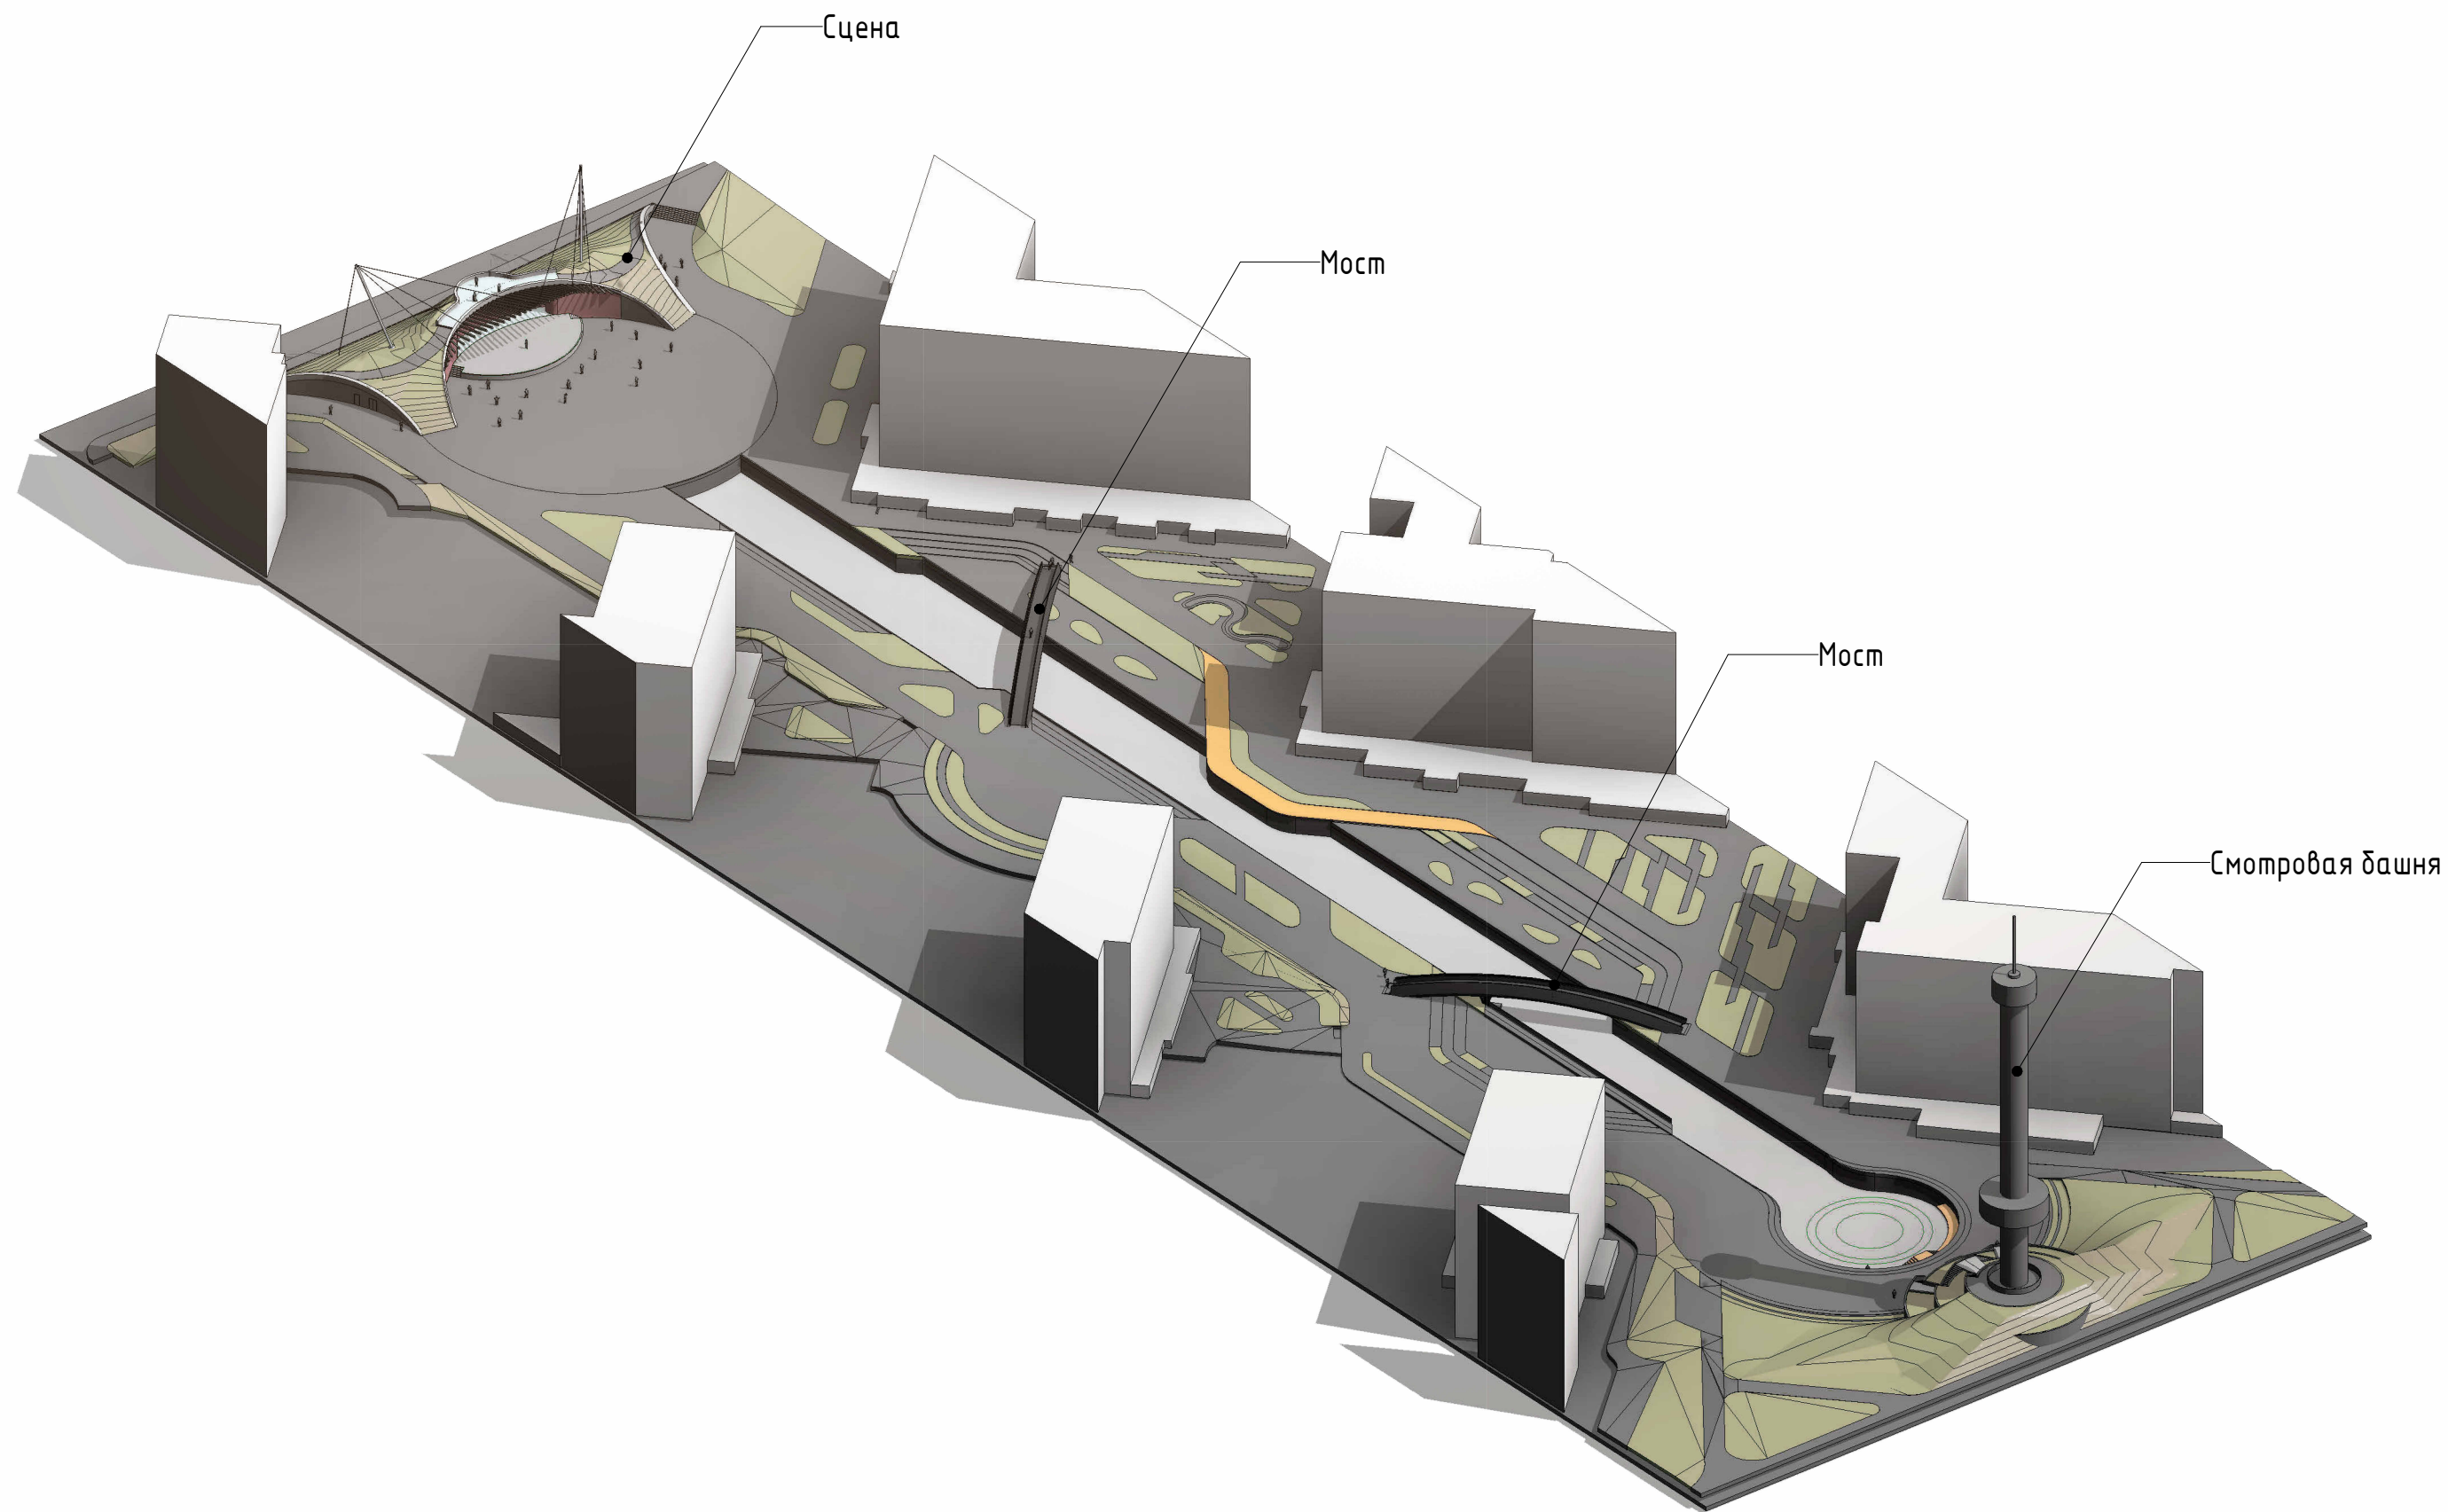

РАСПОЛОЖЕНИЕ ОБЪЕКТОВ

АРХИТЕКТУРНАЯ
ДОКУМЕНТАЦИЯ

05